
CAB · FRONT


Tỉ lệ 1:7.5



HP LAYOUT PRO - DEMO	GIÁM ĐỐC	TÊN CÔNG TRÌNH	TÊN BẢN VẼ	BẢN VẼ SỐ	GHI CHÚ
		MO PHONG KHUNG VA GHEP SCENE	1 TRANG / 1 VIEW - CAB_Front	KT-001	DU LIEU MO PHONG / SYNTHETIC
	GS THI CÔNG	ĐỊA ĐIỂM	HẠNG MỤC	NGÀY	
				15/10/2026	

CAB · RIGHT


Tỉ lệ 1:7.5



HP LAYOUT PRO - DEMO	GIÁM ĐỐC	TÊN CÔNG TRÌNH	TÊN BẢN VẼ	BẢN VẼ SỐ	GHI CHÚ
		MO PHONG KHUNG VA GHEP SCENE	1 TRANG / 1 VIEW - CAB_Right	KT-002	DU LIEU MO PHONG / SYNTHETIC
	GS THI CÔNG	ĐỊA ĐIỂM	HẠNG MỤC	NGÀY	
				15/10/2026	

WARD · SECF 1


Tỉ lệ 1:13.1



HP LAYOUT PRO - DEMO	GIÁM ĐỐC	TÊN CÔNG TRÌNH	TÊN BẢN VẼ	BẢN VẼ SỐ	GHI CHÚ
		MO PHONG KHUNG VA GHEP SCENE	1 TRANG / 1 VIEW - WARD_SecF1	KT-003	DU LIEU MO PHONG / SYNTHETIC
	GS THI CÔNG	ĐỊA ĐIỂM	HẠNG MỤC	NGÀY	
				15/10/2026	

WARD · SECR 1

Tỉ lệ 1:13.1



HP LAYOUT PRO - DEMO	GIÁM ĐỐC	TÊN CÔNG TRÌNH	TÊN BẢN VẼ	BẢN VẼ SỐ	GHI CHÚ
		MO PHONG KHUNG VA GHEP SCENE	1 TRANG / 1 VIEW - WARD_SecR1	KT-004	DU LIEU MO PHONG / SYNTHETIC
	GS THI CÔNG	ĐỊA ĐIỂM	HẠNG MỤC	NGÀY	
				15/10/2026	